



Photo 01



Photo 02



Photo 05



Photo 03 après Insertion



Photo 03 avant Insertion



Photo 04 après Insertion



Photo 04 avant Insertion

CODIF : P.C.

DATE :

VISA CLIENT :

VISA DIRECTION :

ZAC "DES BEGNENNES" - Lot n°05- 57365 ENNERY

PCMI 2

Plan de masse

TRAVAUX A CHARGE
CLIENT :

- Murets
- Plantations
- Clôture(s)
- Branchements
- Cariveau(x) bas de rampe
- Evacuation des terres
- Frais de décharge
- Bornage à compléter
- Pose compteur d'eau
- -----
- -----

Légende

Eaux Usées

Regard EU

Eaux Pluviales

Regard EP

Eau potable

Compteur AEP

Basse tension

Coffret BT

Téléphone

Coffret Téléphone ☒

Gaz


Coffret Gaz

CODIF : P.C.

DATE :

VISA CLIENT :
avec mention "bon pour implantation"

VISA DIRECTION :

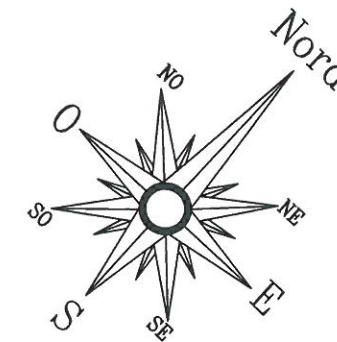

NIVEAUX DIVERS :

Soubassement :

NIV Fond/fouille +1.22
NIV Fond/fondation +1.72
NIV Fond/forme +2.02

COTE GARAGE :

NIV Garage +2.80

COTE HABITABLE :

NIV Terrasse +2.78

NIV RDC +2.98

NIV Egout Bas +5.55

NIV Faîtage Bas +8.1

NIV Egout Haut +8.3

NIV Faîtage Haut +1

Page 10 of 10

FE EU +/-0.00
REFERENCE

NIVEAU VOIE PUBLIQUE,
FINIE SUPPOSÉE +2.75

NIVEAU VOIE PUBLIQUE
FINIE SUPPOSÉE +2.76

NIVEAU VOIE PUBLIQUE /
FINIE SUPPOSÉE +2.82

FE +1.60/

NIVEAU VOIE PUBLIQUE
FINIE SUPPOSÉE +2.83


Branchements :
Emplacements supposés sur domaine public
(Cf. certificat administratif de viabilité)

Échelle 1/200

0.00 ml 10.00 ml


* Les éléments d'aménagement extérieur présentés sur ce document, ne sont pas opposables au constructeur qui n'en assure pas la réalisation, sauf stipulation contractuelle contraire. En aucun cas, la responsabilité du constructeur, ne pourra être recherchée en cas de refus de délivrance de conformité pour non conformité des aménagements extérieurs dont le maître d'ouvrage reste responsable de l'exécution. *

FACADE SUD EST

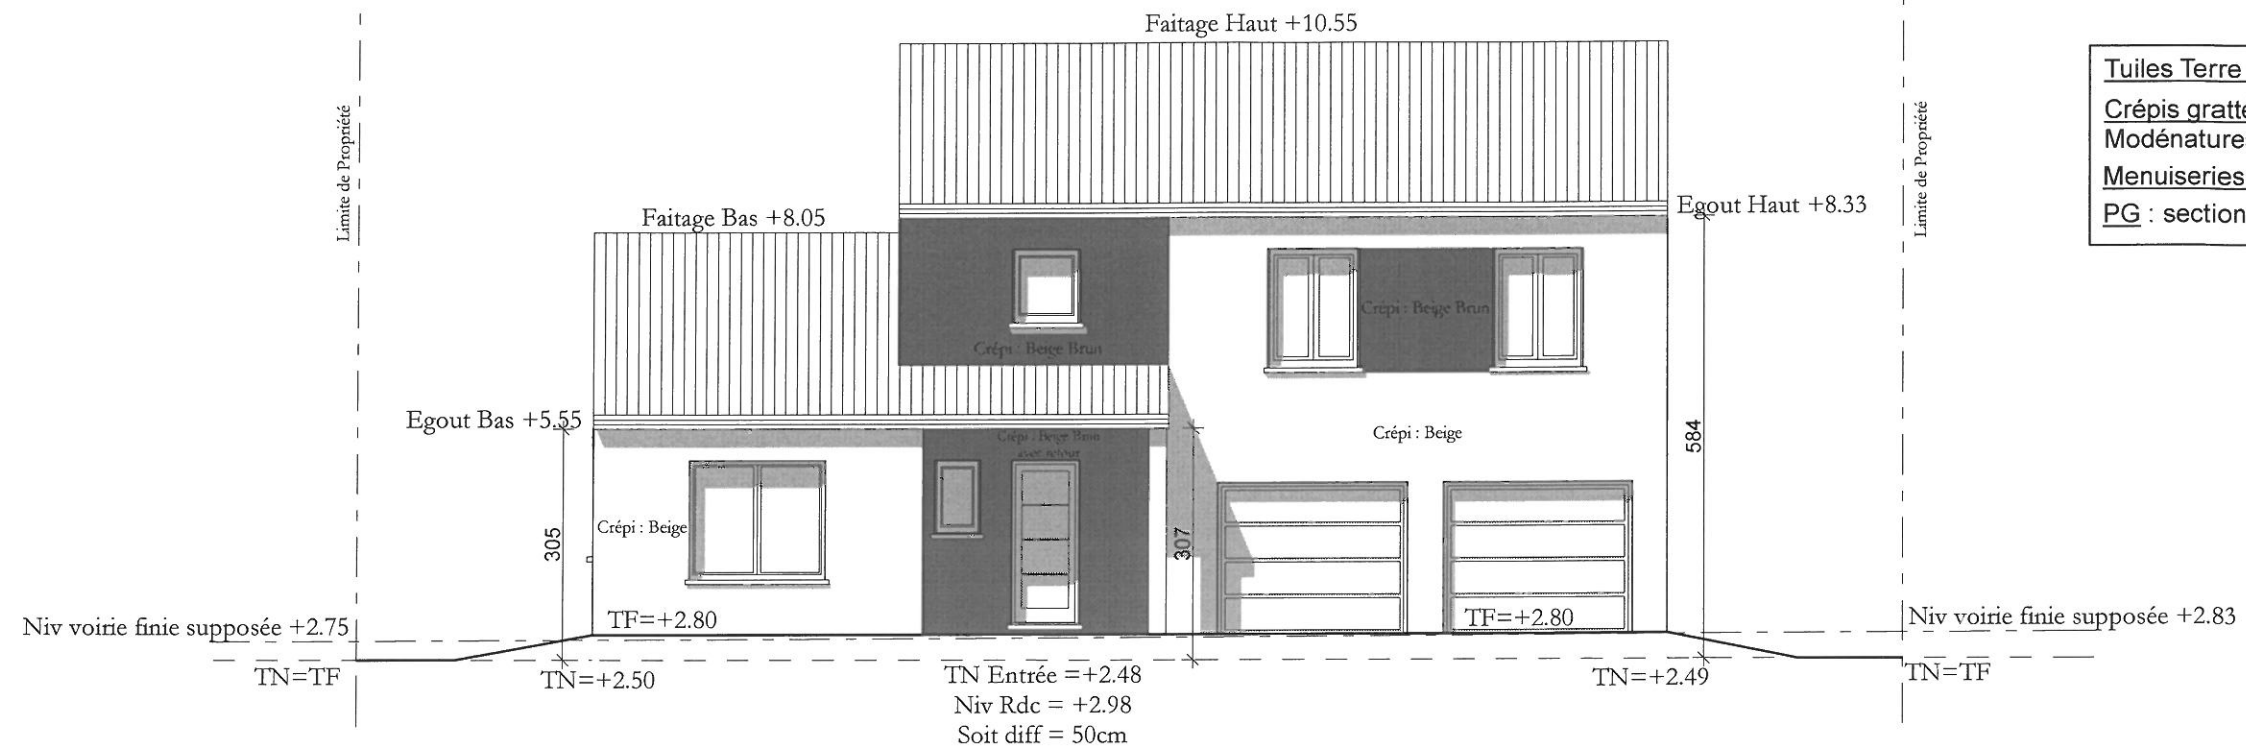

Tuiles Terre Cuite : PRIMA Rouge Flamée
Crépis gratté : Principale BEIGE
 Modénatures BEIGE BRUN
Menuiseries PVC : Blanches
PG : sectionnelle à lames horizontales "L"


FACADE NORD OUEST

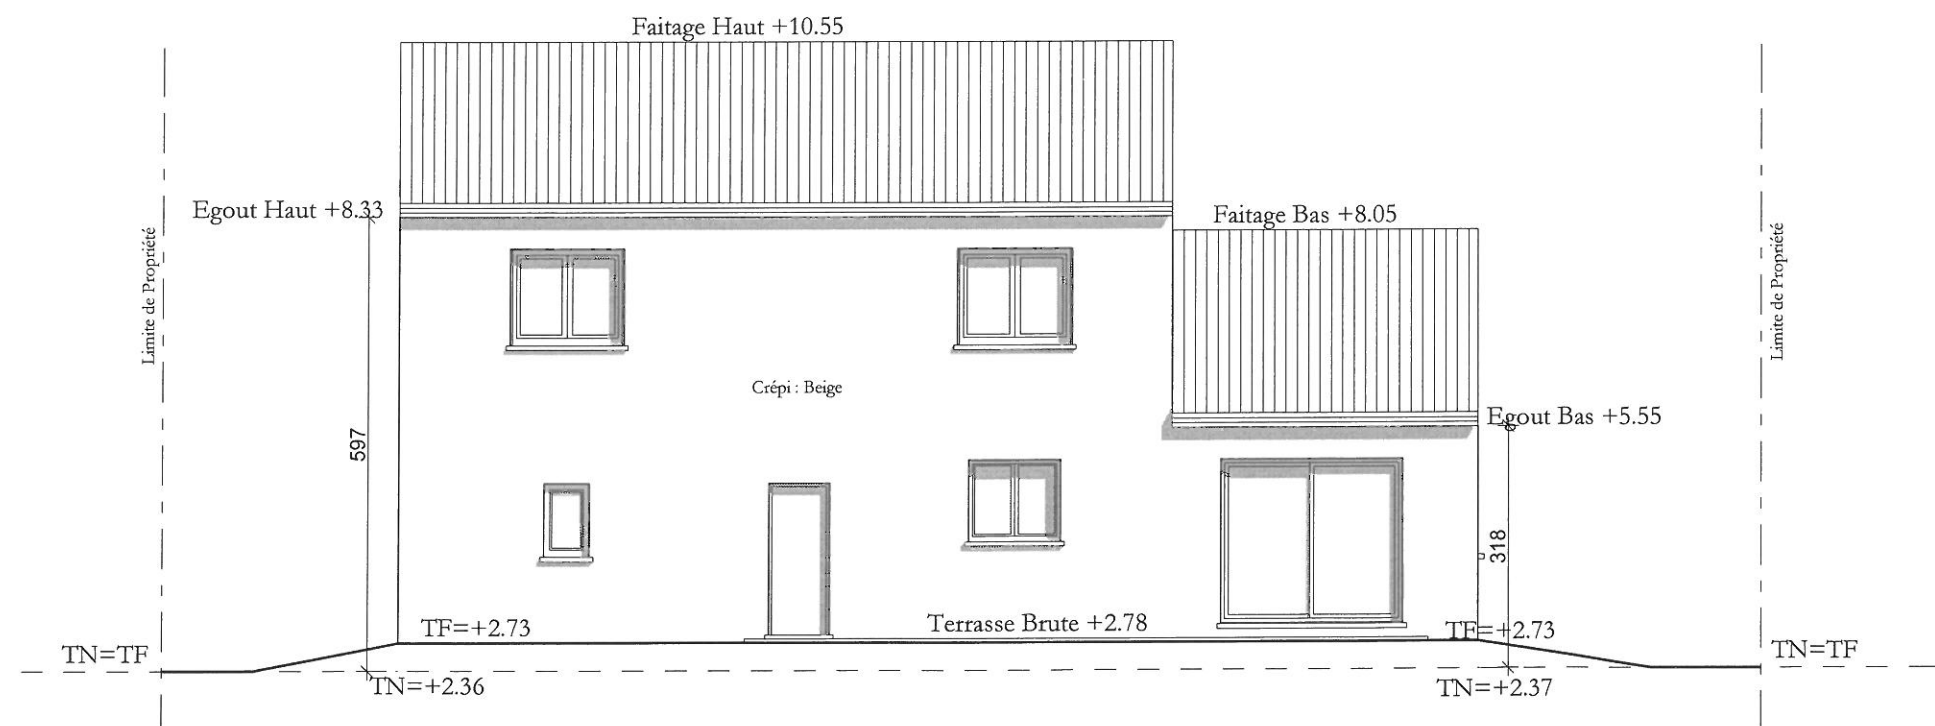


CODIF. :	PC
DATE :	
VISA CLIENT	
VISA DIRECTION	

FACADES
Echelle 1/100

PIGNON SUD OUEST

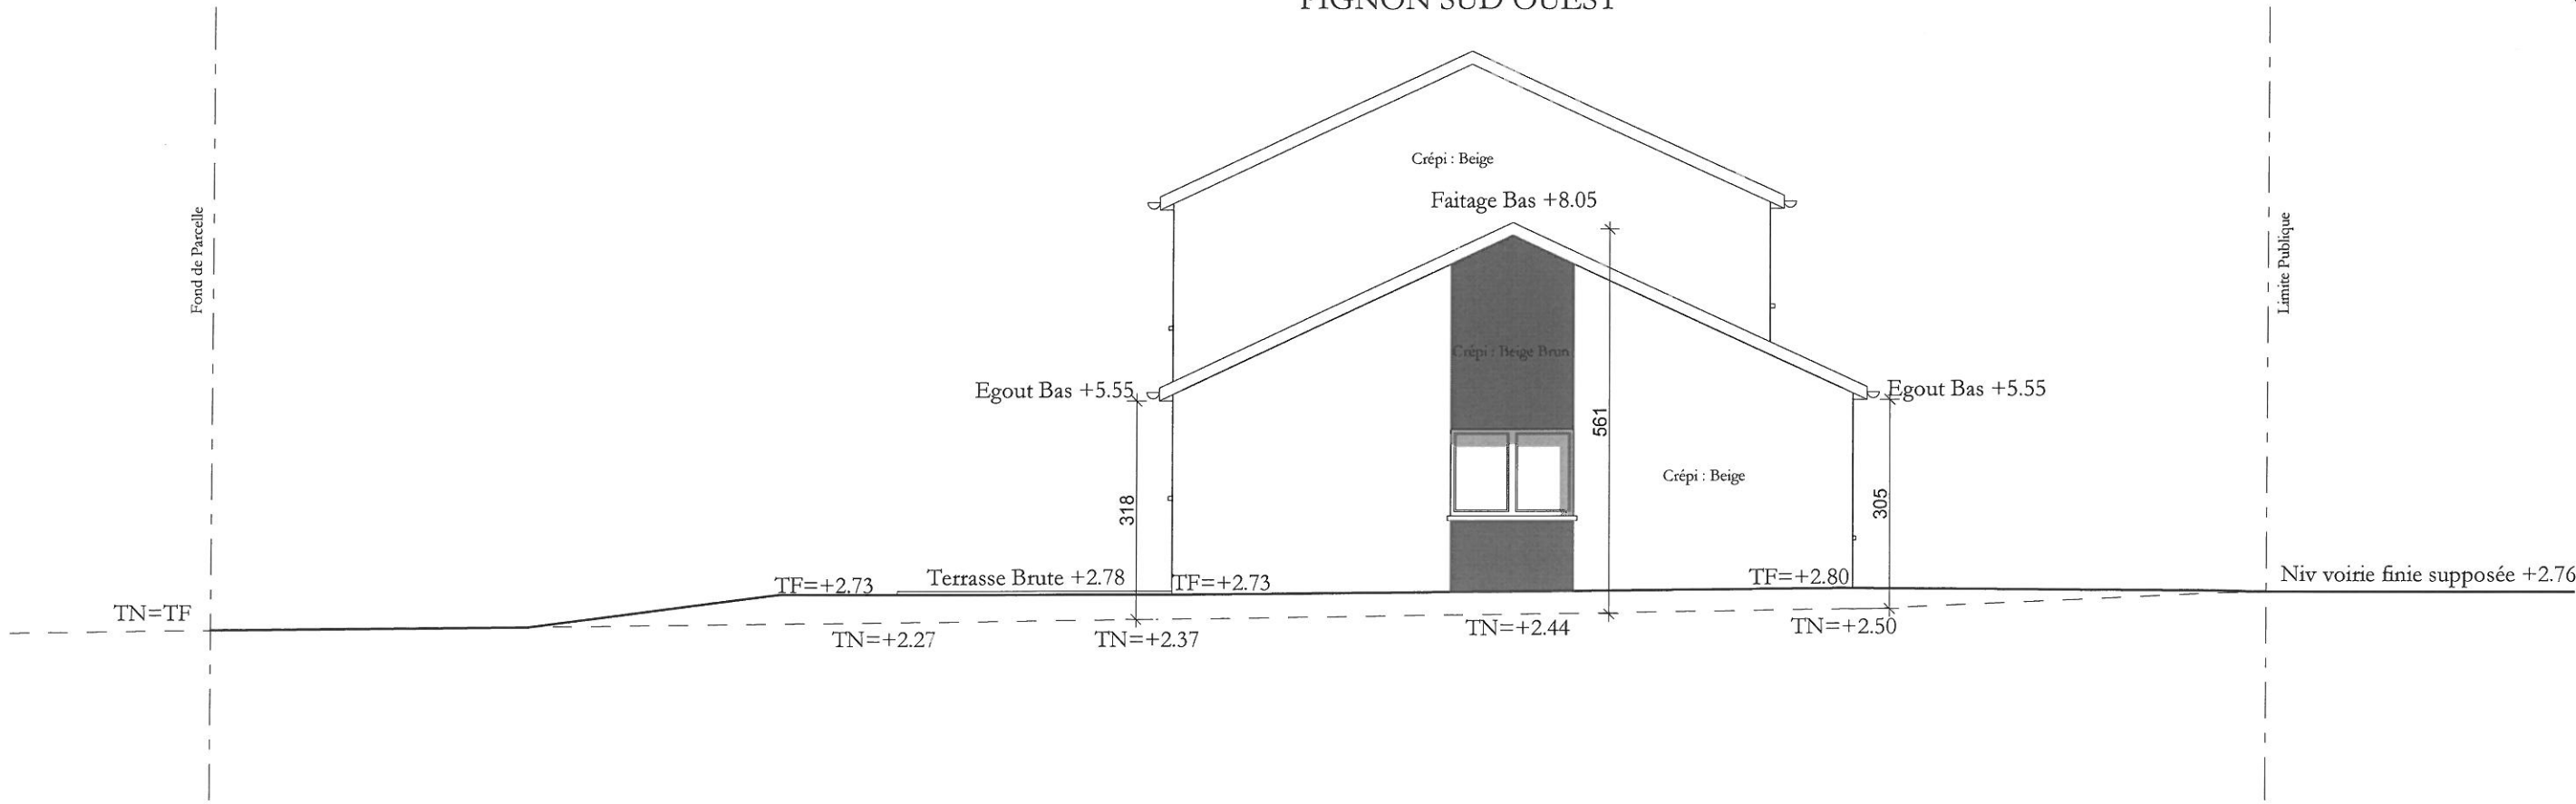


PIGNON NORD EST

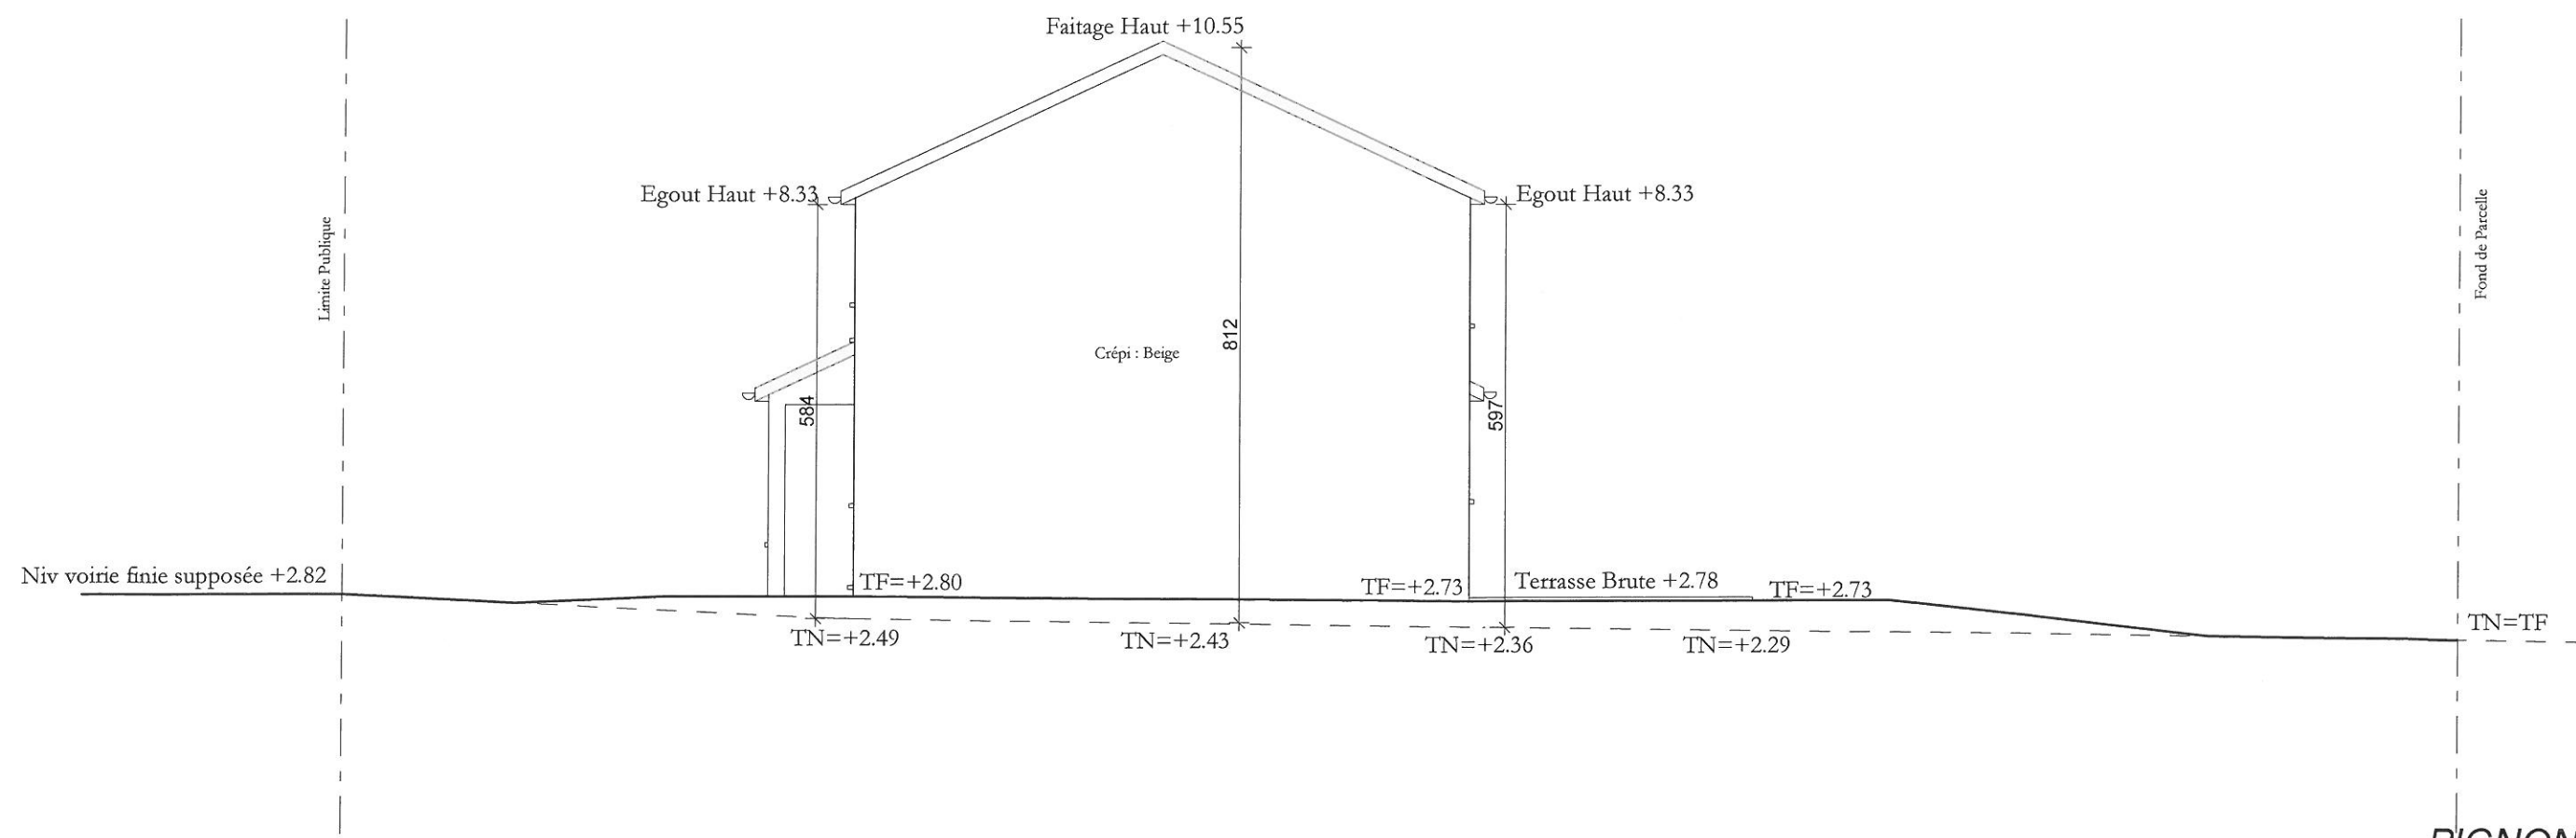

PIGNONS
Echelle 1/100


CODIF. :	PC
DATE :	
VISA CLIENT	
VISA DIRECTION	

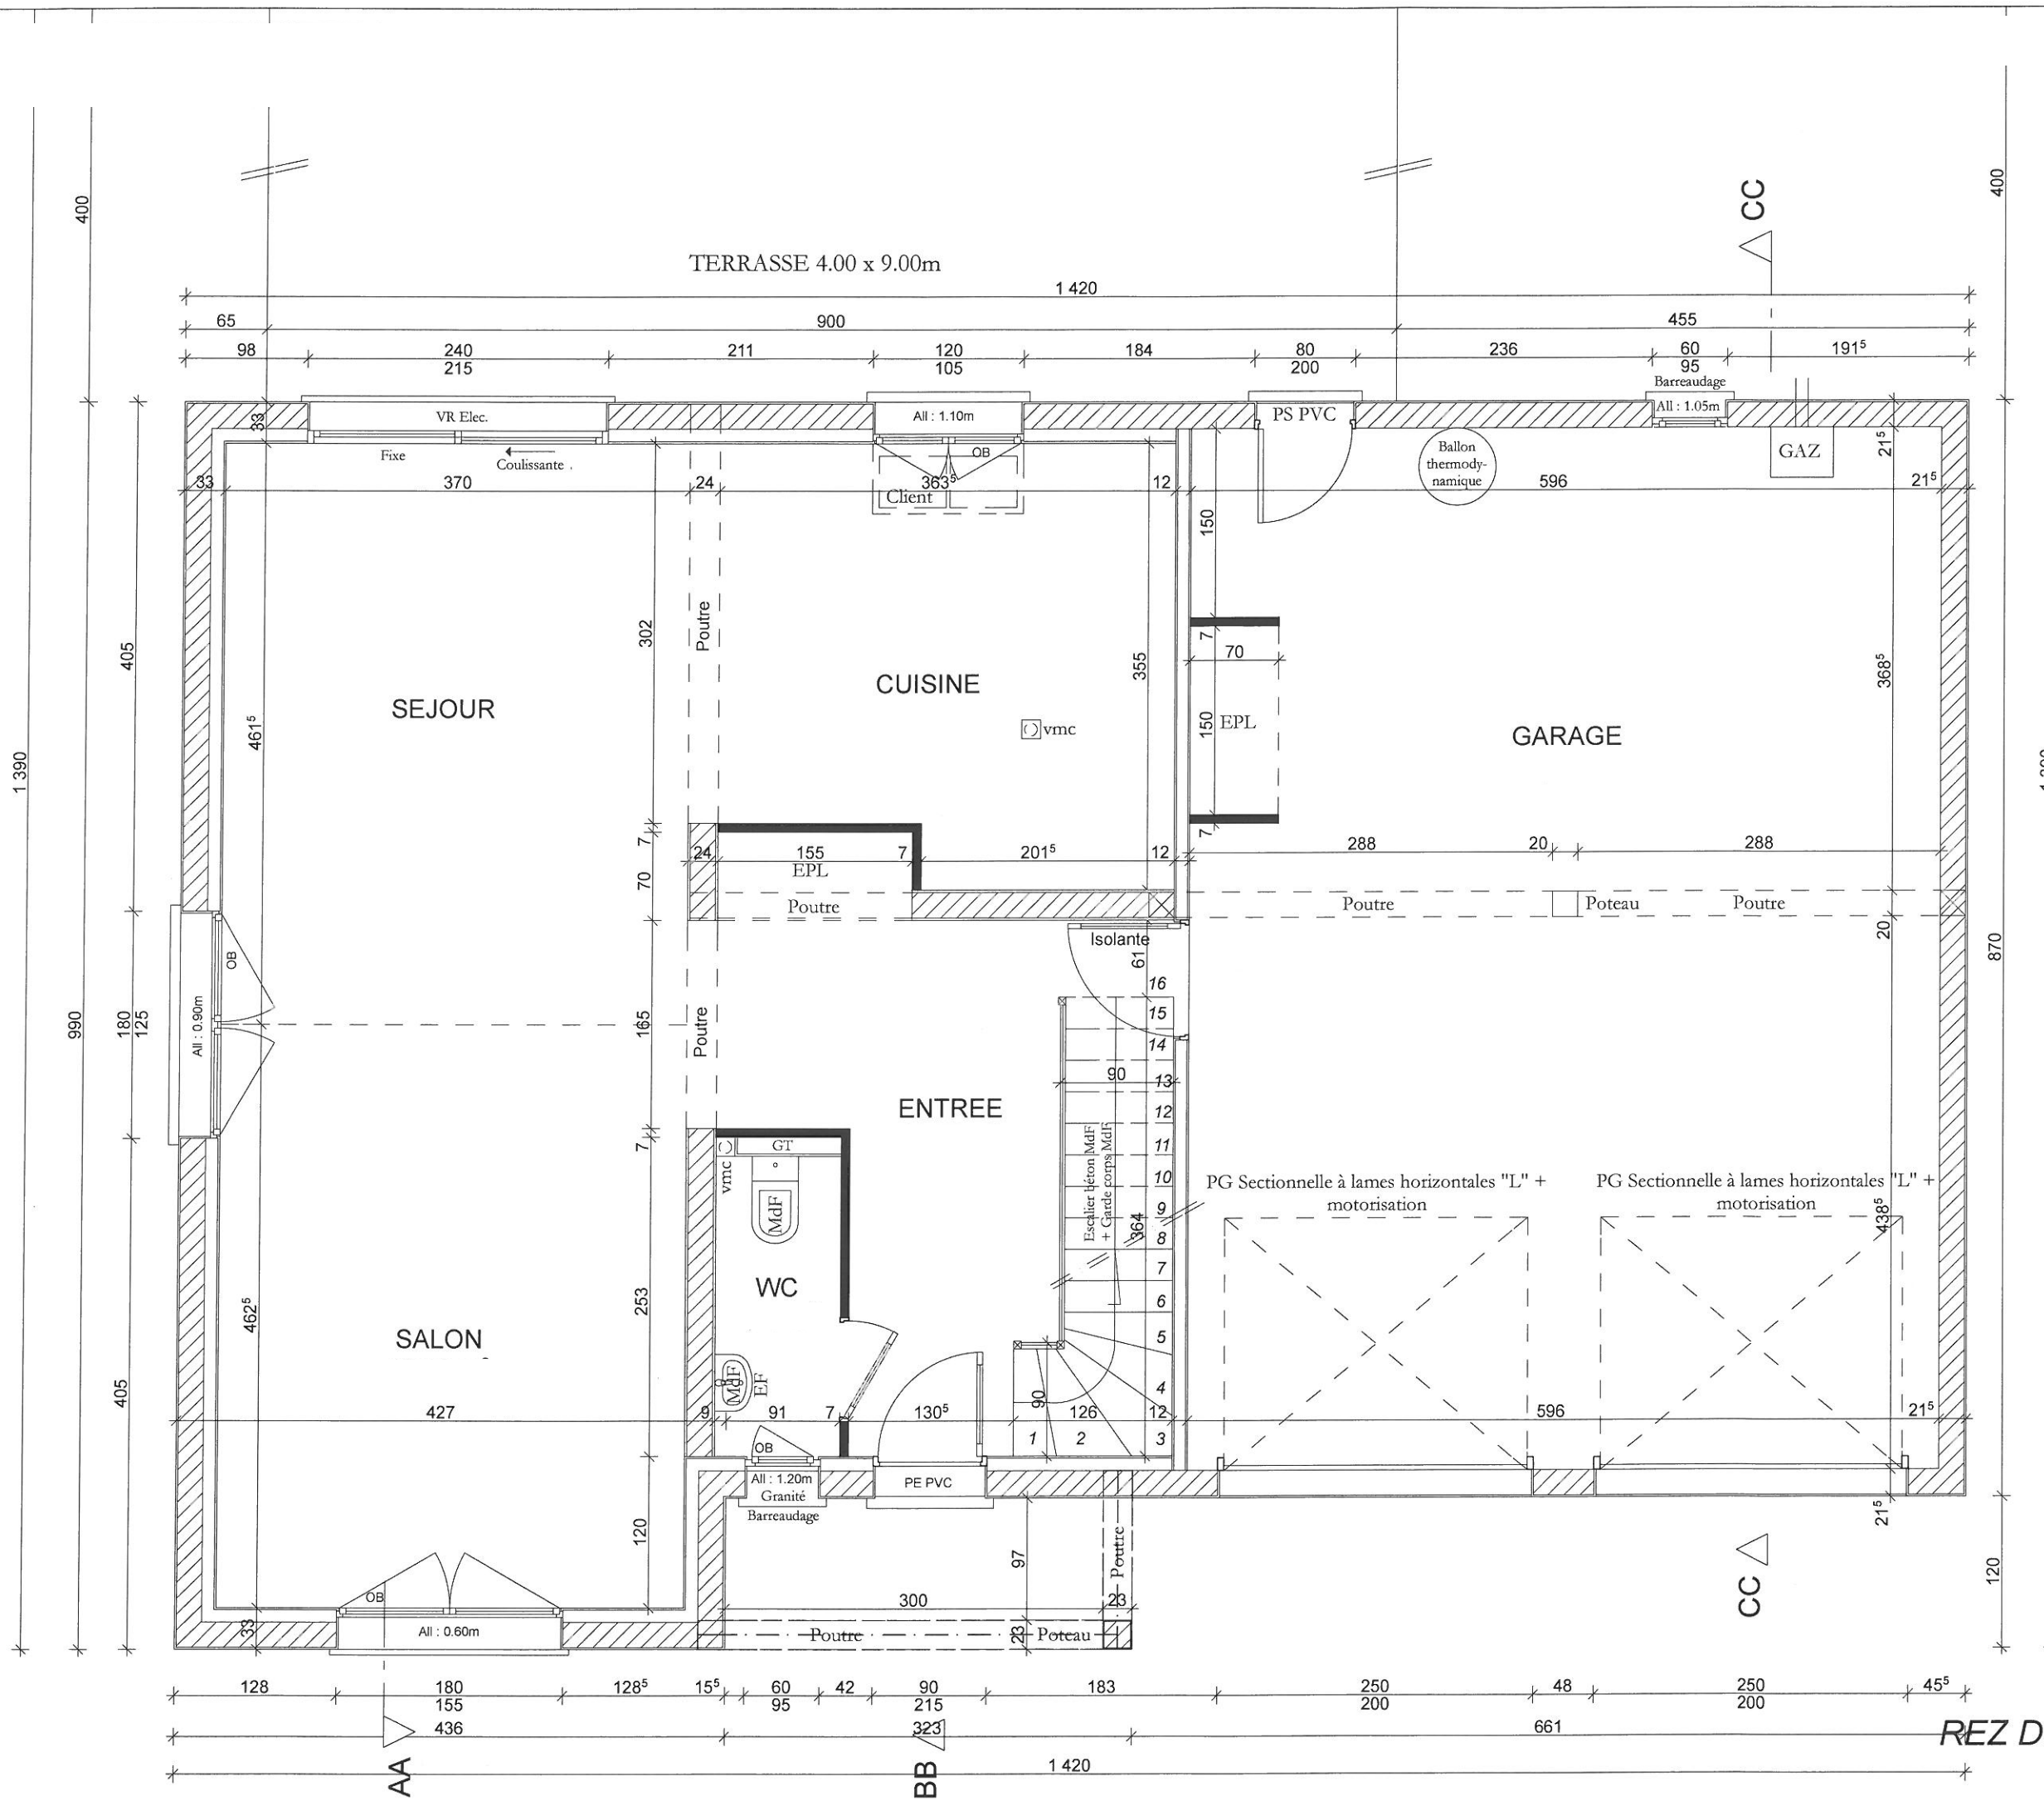

S.H: 60.92 m²

CODIF. :	PC
DATE :	
VISA CLIENT	
VISA DIRECTION	

REZ DE CHAUSSEE
Echelle 1/50

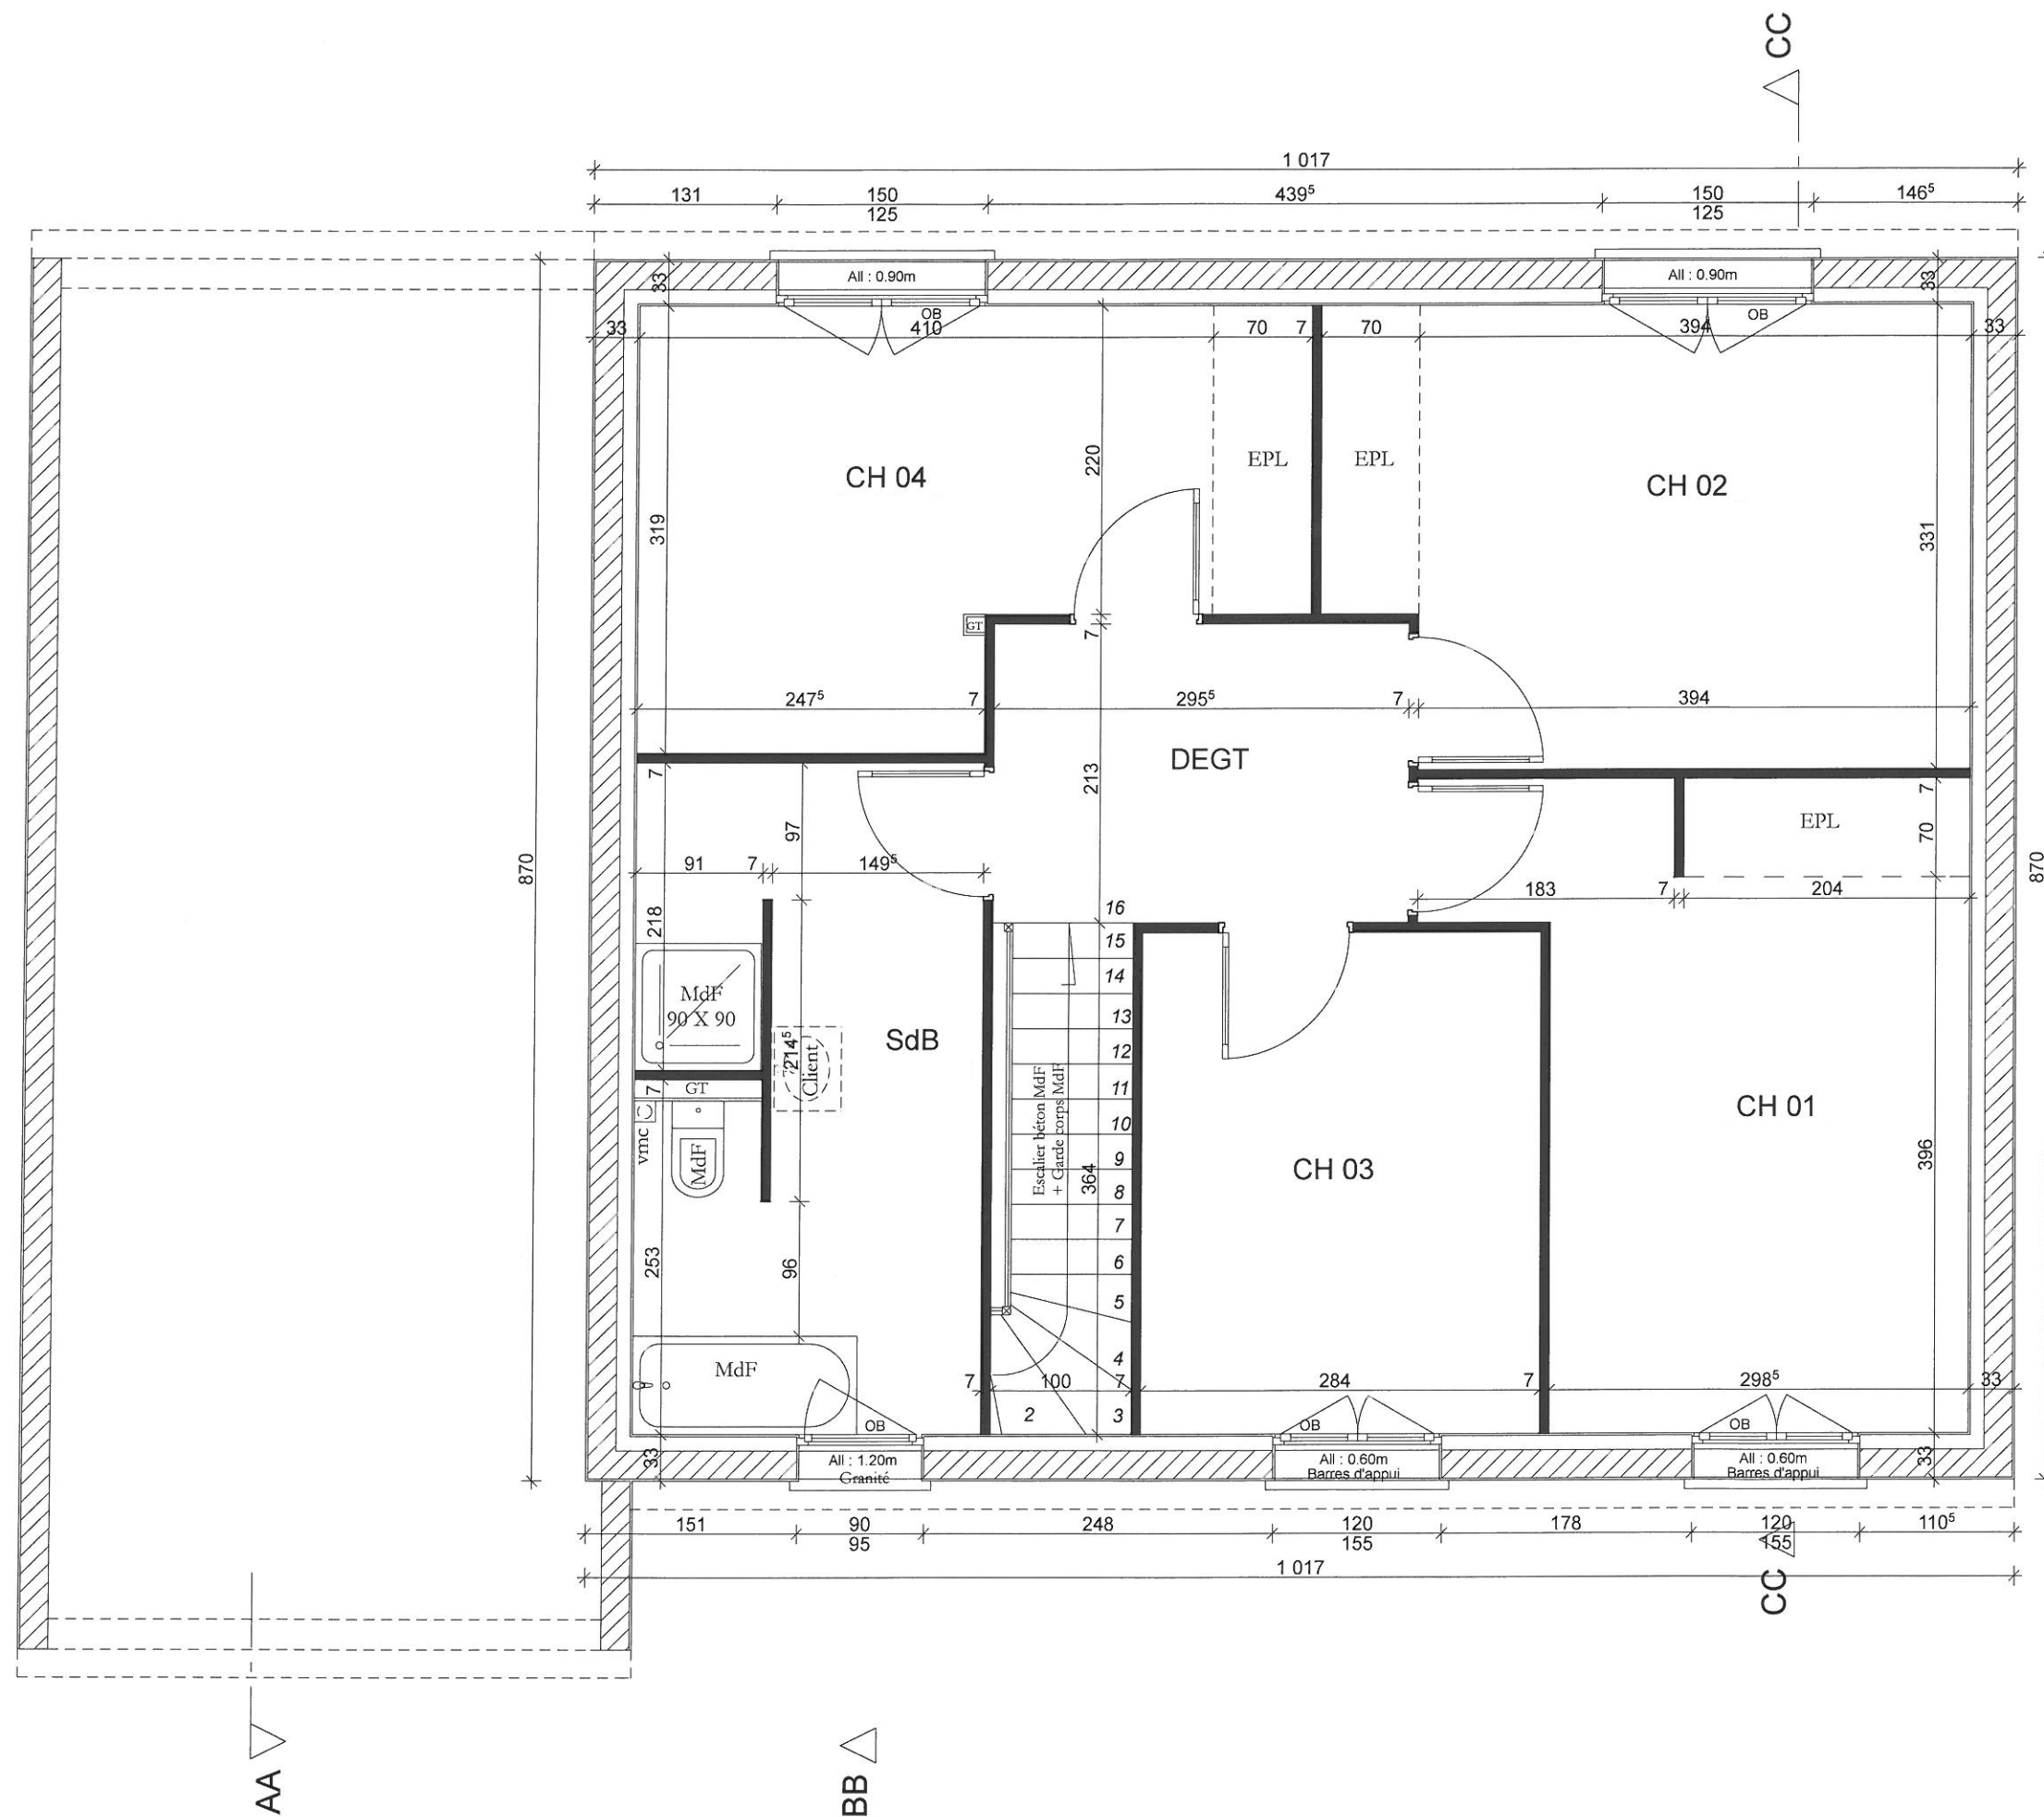

S.H: 70.33 m²

CODIF. : PC

DATE :

VISA CLIENT

VISA DIRECTION

ETAGE
Echelle 1/50